




Concrete floor

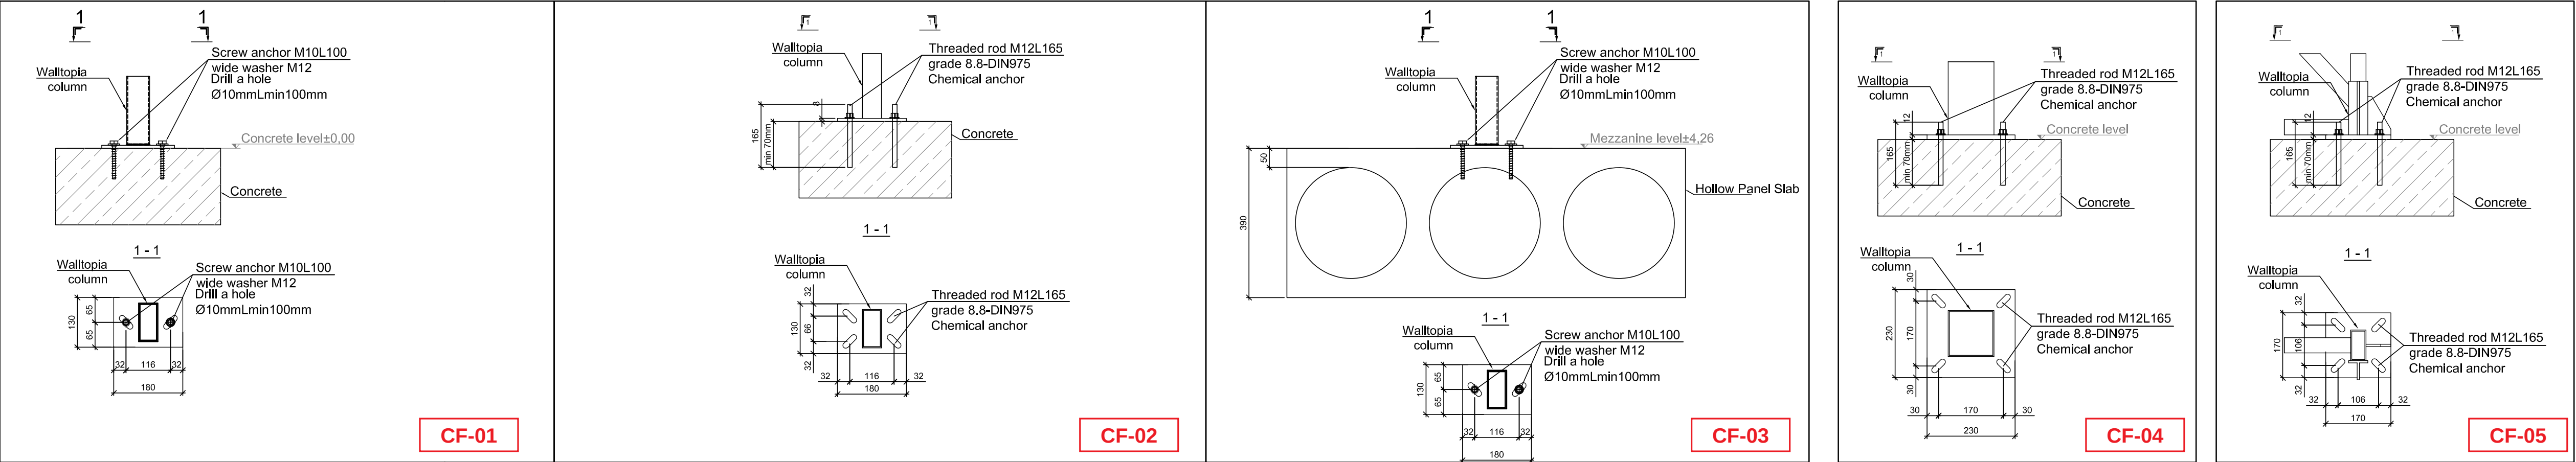


Concrete wall

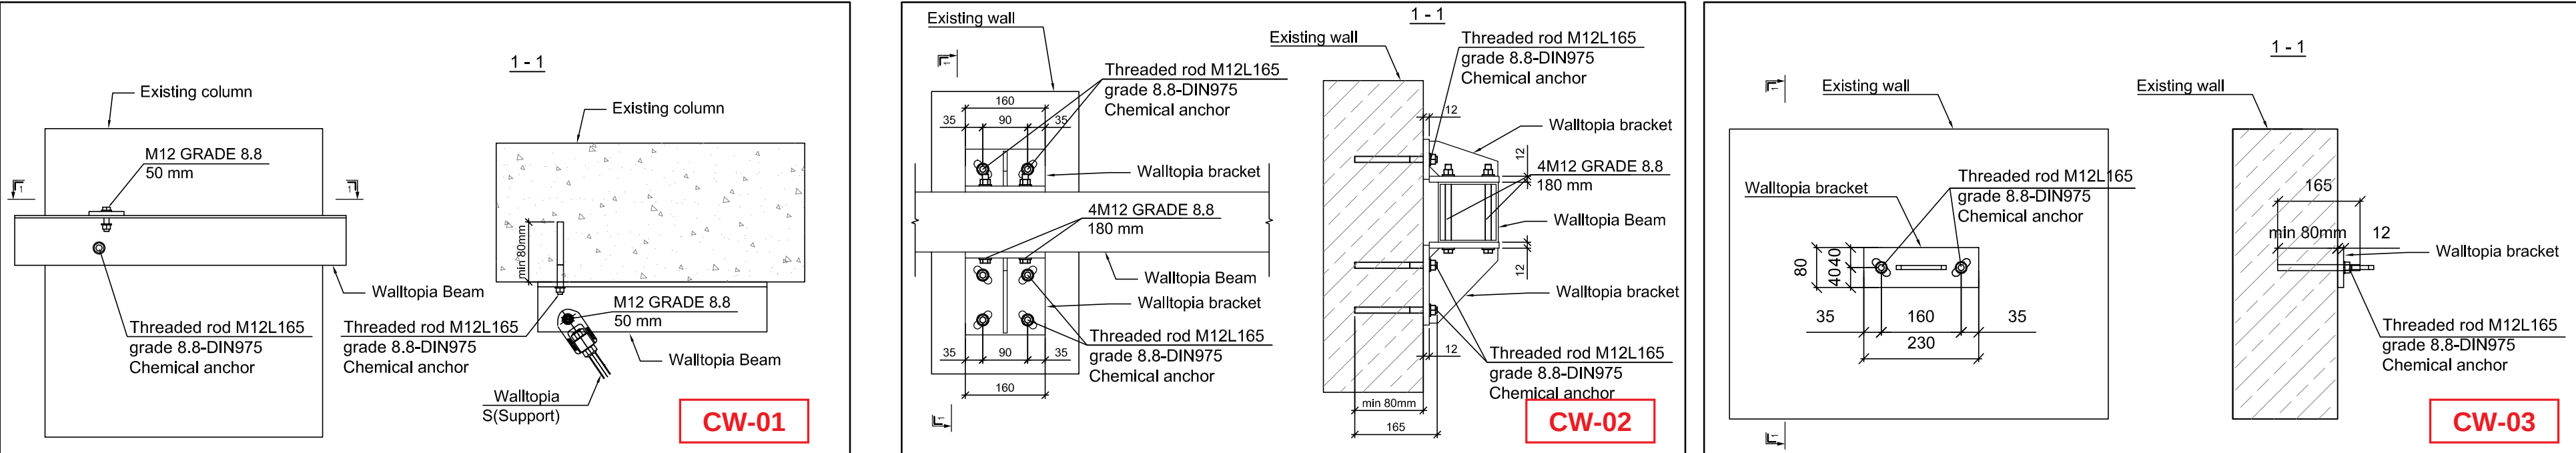


Steel column

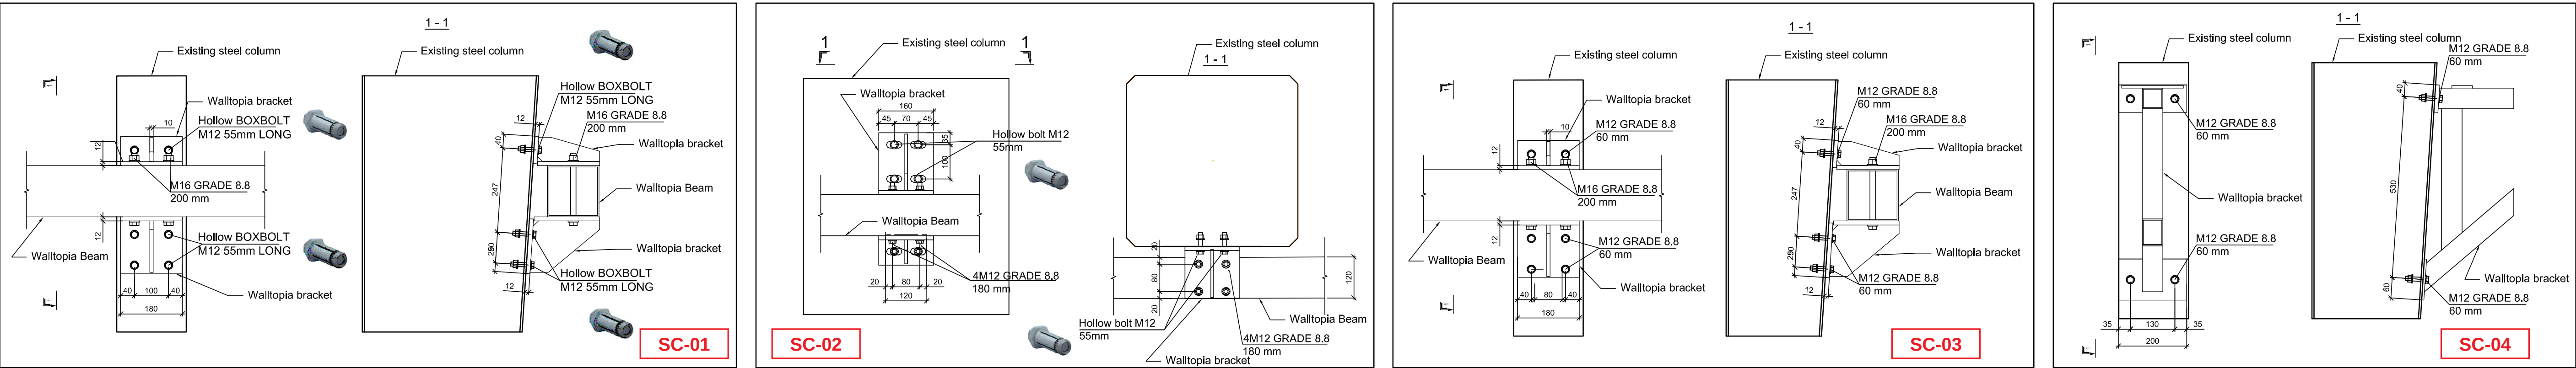

Steel beam

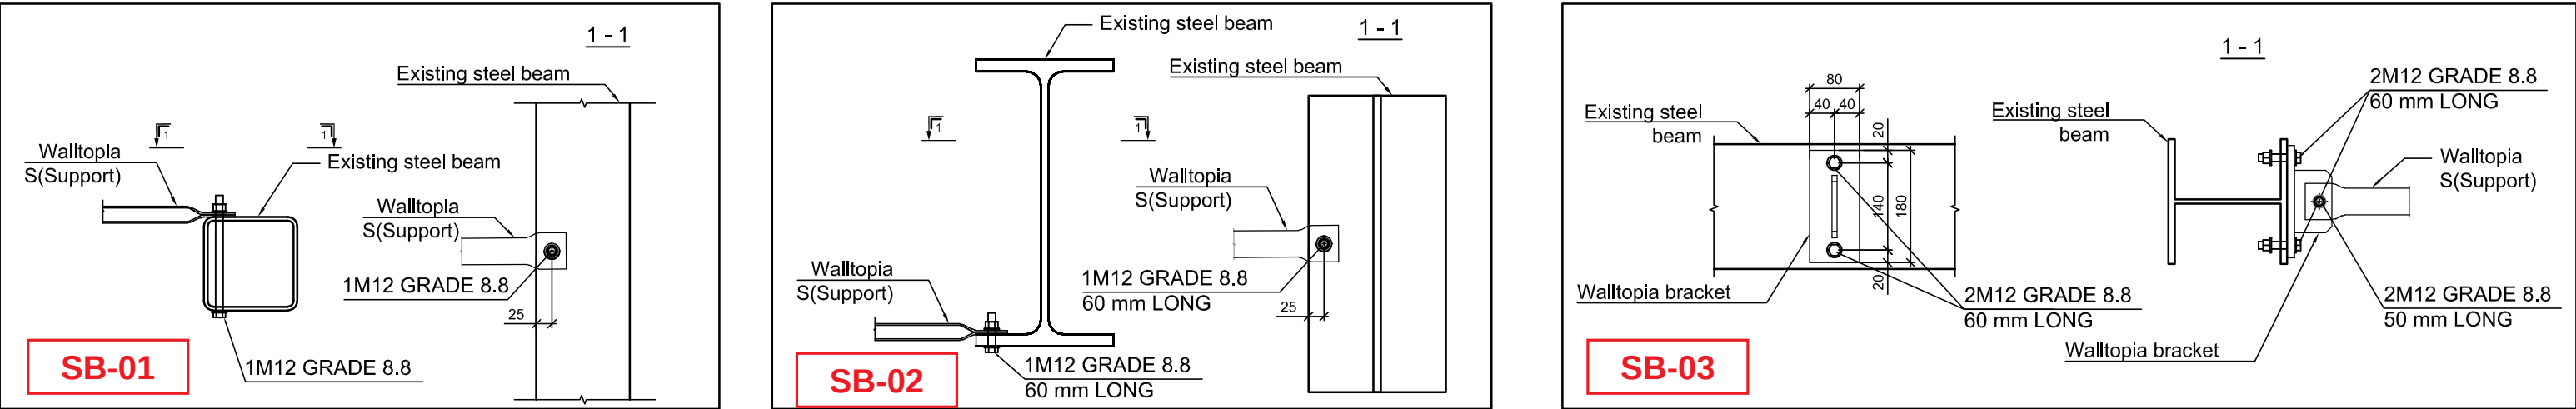

Masonry wall

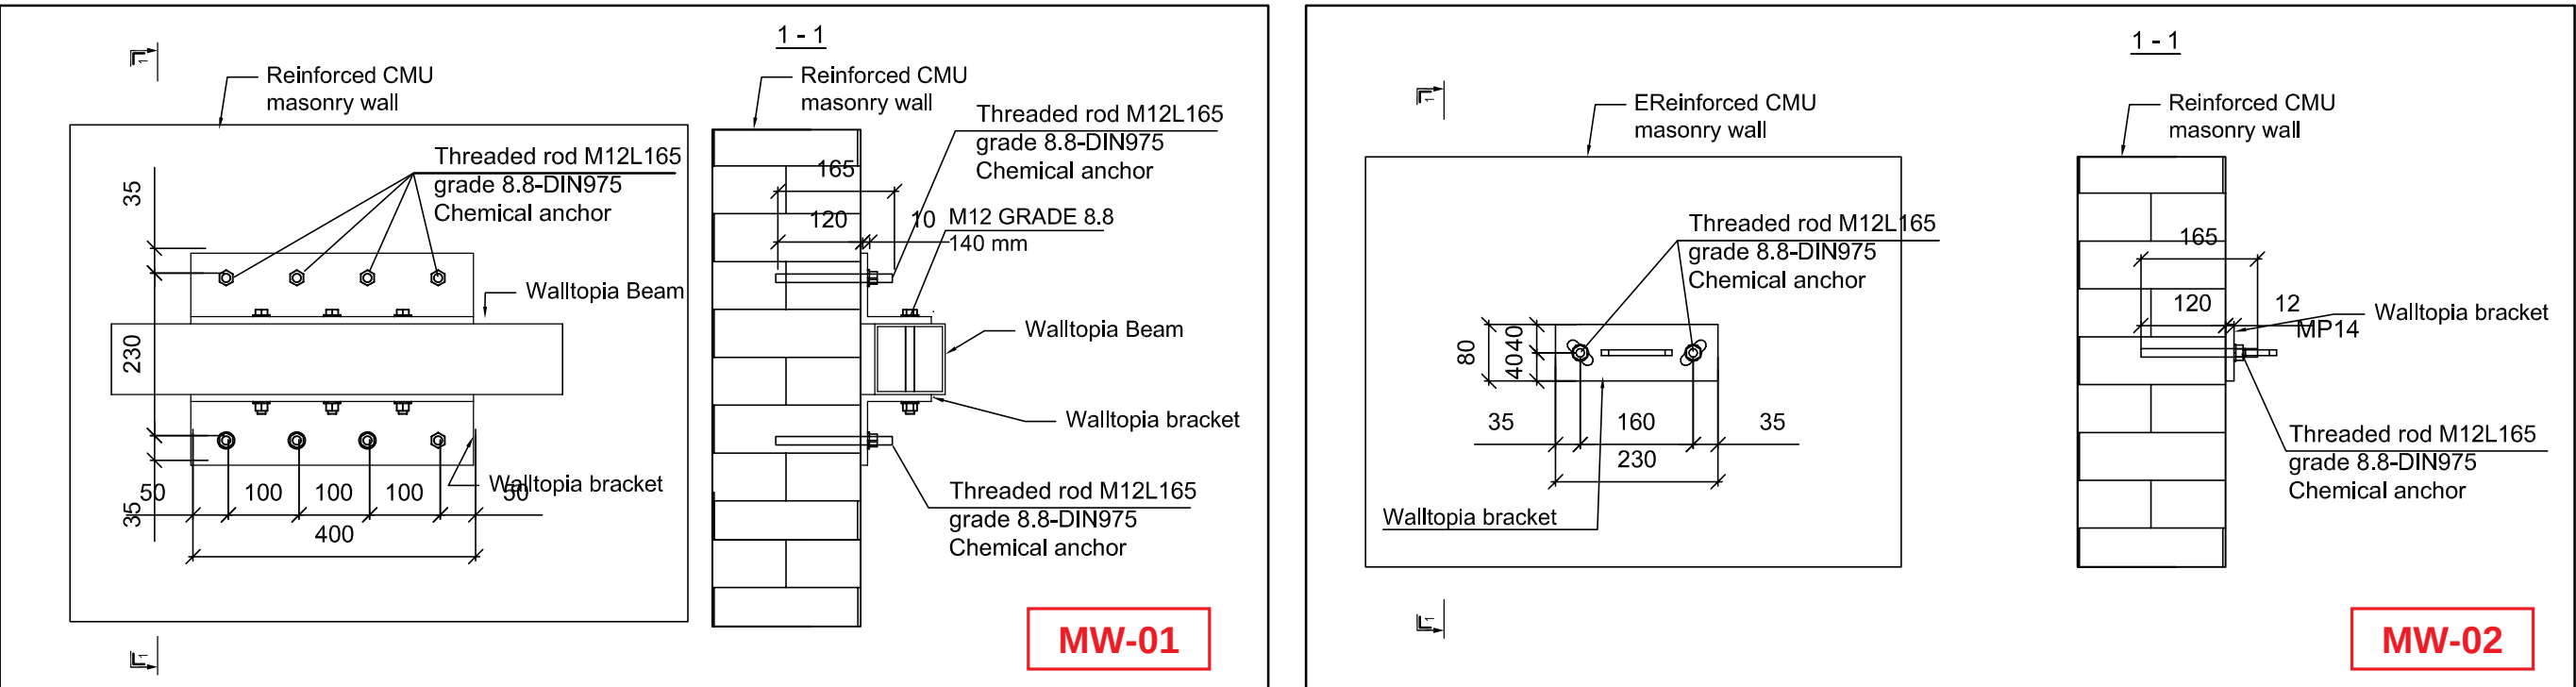

REVISIONS:	
No.	Date
All plans, engineering drawings, designs, images, trademarks and any other objects of IP are property of Walltopia AD and may not be used, duplicated, reproduced, modified, and/or distributed, in whole or in part, without the explicit written consent of Walltopia AD.	

CLIENT:

Country - City - Name

Walltopia
Standard
Anchoring details
metric

DRAWN: ENG.B.Stoyanov
CHECKED: ENG.P.PETROV
SCALE: 1:10 Format: A1
PROJECT NO.: T1-XXXX
SHEET: S10X
DRAWING: XX